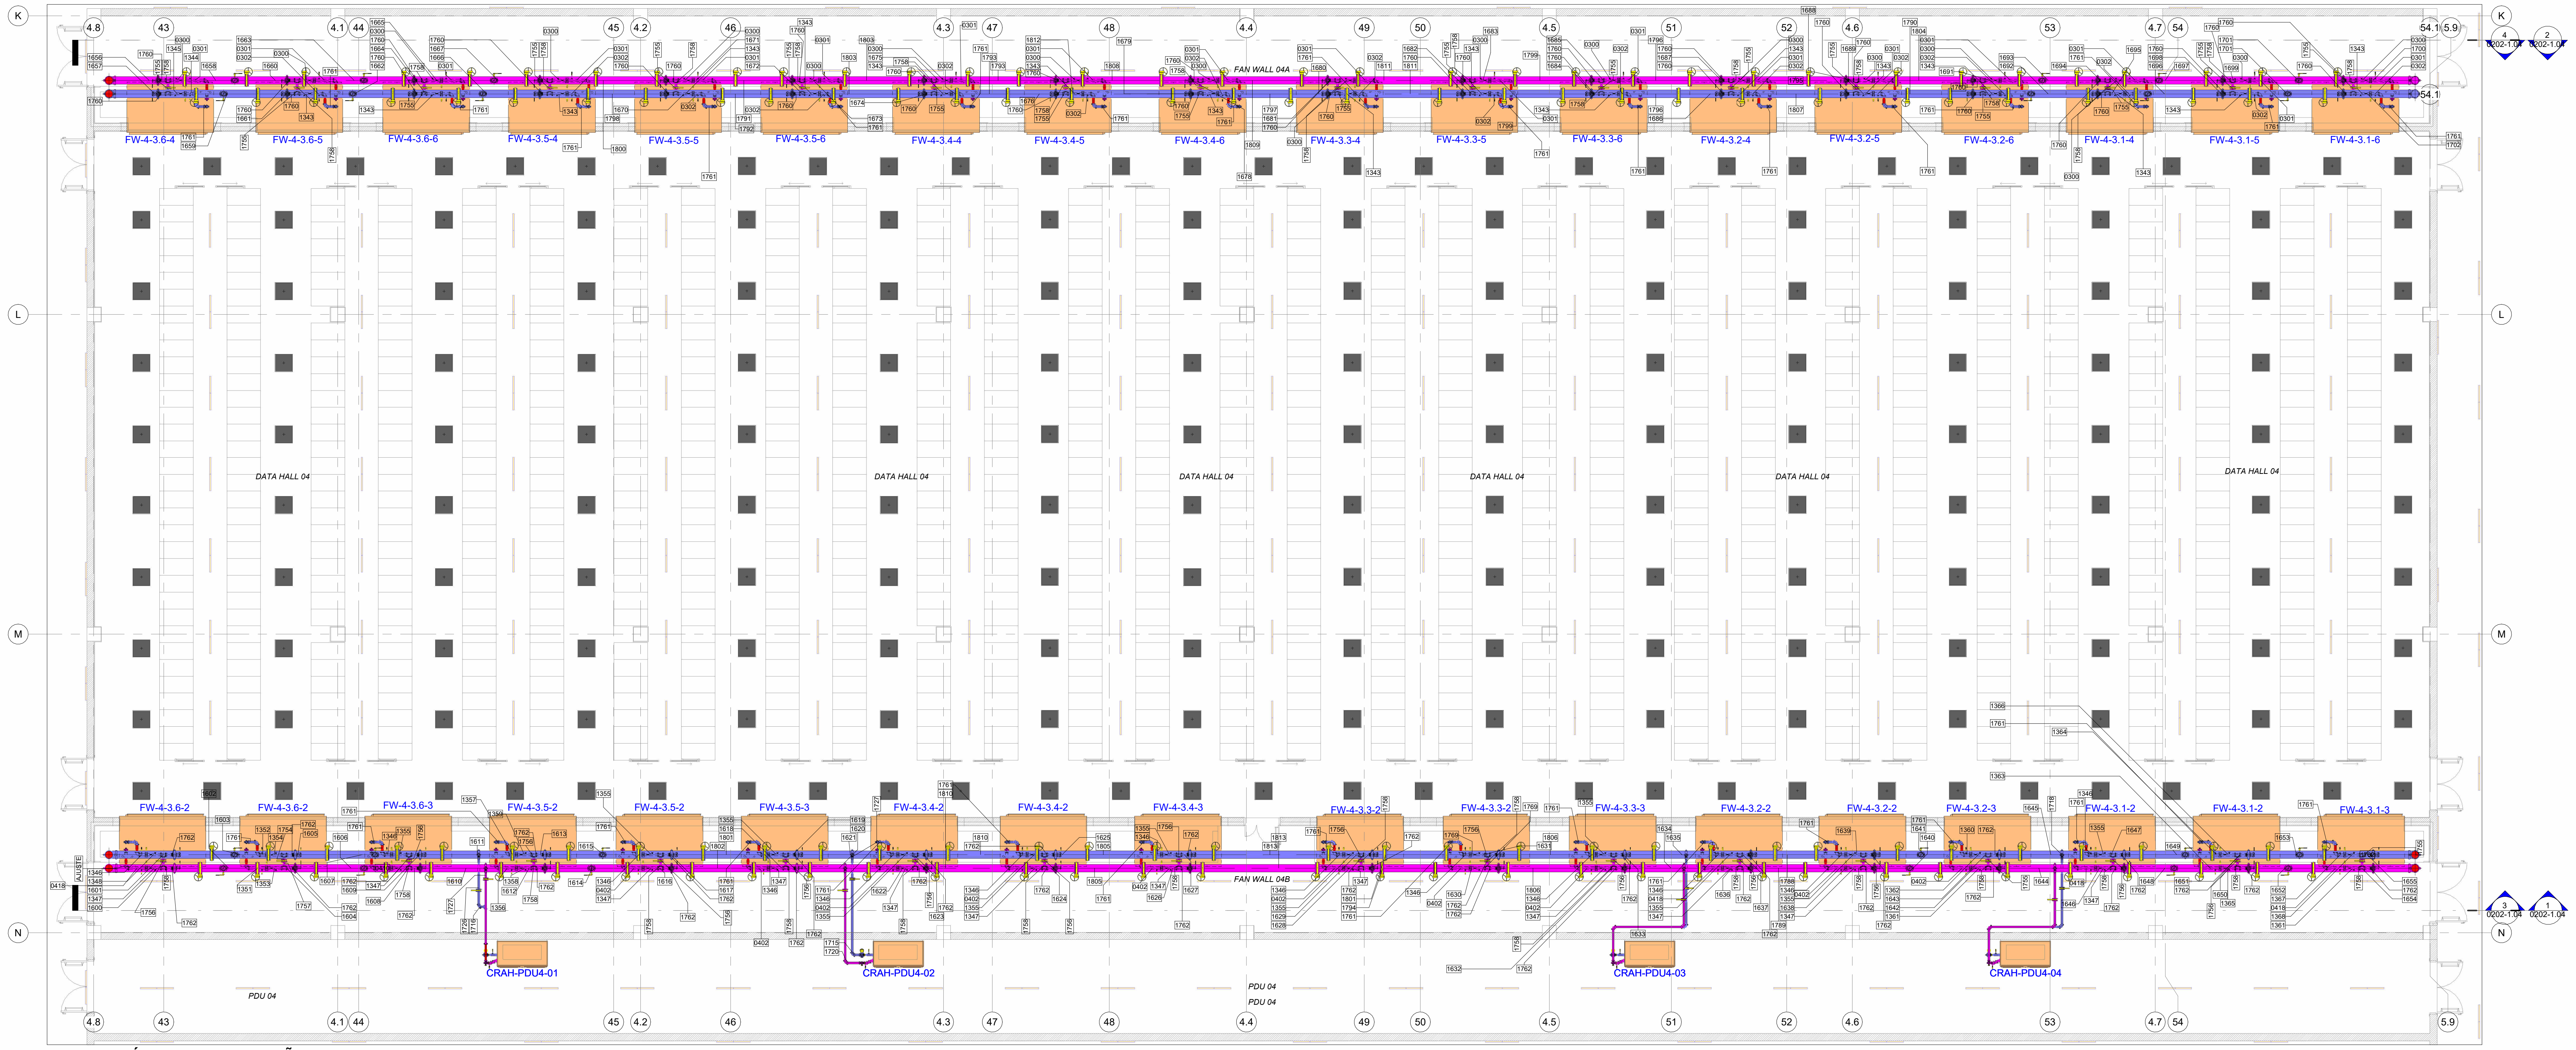
K
L
M
N
4.8
43
4.1
44
45
4.2
46
4.3
47
48
4.4
49
50
4.5
51
52
4.6
53
4.7
54
54.1
5.9
FAN WALL 04A
FAN WALL 04B
DATA HALL 04
PDU 04
FW-4-3.6-4
FW-4-3.6-5
FW-4-3.6-6
FW-4-3.5-4
FW-4-3.5-5
FW-4-3.5-6
FW-4-3.4-4
FW-4-3.4-5
FW-4-3.4-6
FW-4-3.3-4
FW-4-3.3-5
FW-4-3.3-6
FW-4-3.2-4
FW-4-3.2-5
FW-4-3.2-6
FW-4-3.1-4
FW-4-3.1-5
FW-4-3.1-6
FW-4-3.6-2
FW-4-3.6-2
FW-4-3.6-3
FW-4-3.5-2
FW-4-3.5-2
FW-4-3.5-3
FW-4-3.4-2
FW-4-3.4-2
FW-4-3.4-3
FW-4-3.3-2
FW-4-3.3-2
FW-4-3.3-3
FW-4-3.2-2
FW-4-3.2-2
FW-4-3.2-3
FW-4-3.1-2
FW-4-3.1-2
FW-4-3.1-3
CRAH-PDU4-01
CRAH-PDU4-02
CRAH-PDU4-03
CRAH-PDU4-04

P — TÉRREO - FABRICAÇÃO DE TUBOS CORREDOR FAN WALL 04 "A" E "B" - SETOR 04

GROUND - PIPE FABRICATION CORRIDOR FANWALL "A" E "B" - SECTOR 03 | 1 : 100

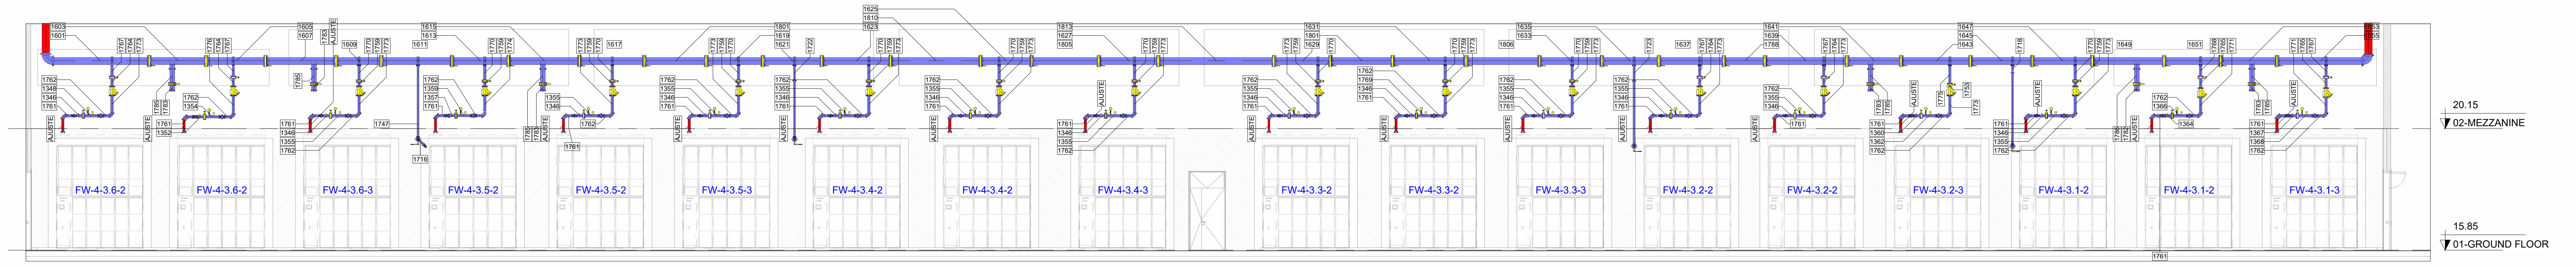
FW-4-3.6-2
FW-4-3.6-2
FW-4-3.6-3
FW-4-3.5-2
FW-4-3.5-2
FW-4-3.5-3
FW-4-3.4-2
FW-4-3.4-2
FW-4-3.4-3
FW-4-3.3-2
FW-4-3.3-2
FW-4-3.3-3
FW-4-3.2-2
FW-4-3.2-2
FW-4-3.2-3
FW-4-3.1-2
FW-4-3.1-2
FW-4-3.1-3
20.15
02-MEZZANINE
15.85
01-GROUND FLOOR

1 — SPO - FAN WALL 03A - AAG - SETOR 04

SPOOLS FAN WALL 03A - CWS - SECTOR 04 | 1 : 100

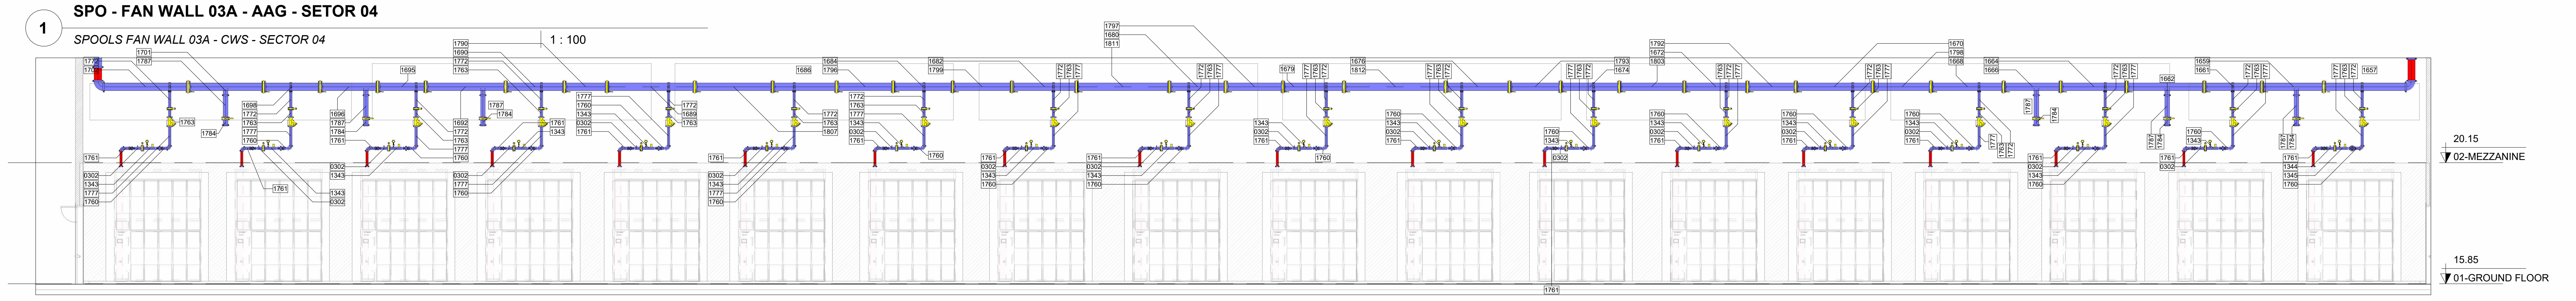
20.15
02-MEZZANINE
15.85
01-GROUND FLOOR

2 — SPO - FAN WALL 03B - AAG - SETOR 04

SPOOLS FAN WALL 03B - CWS - SECTOR 04 | 1 : 100

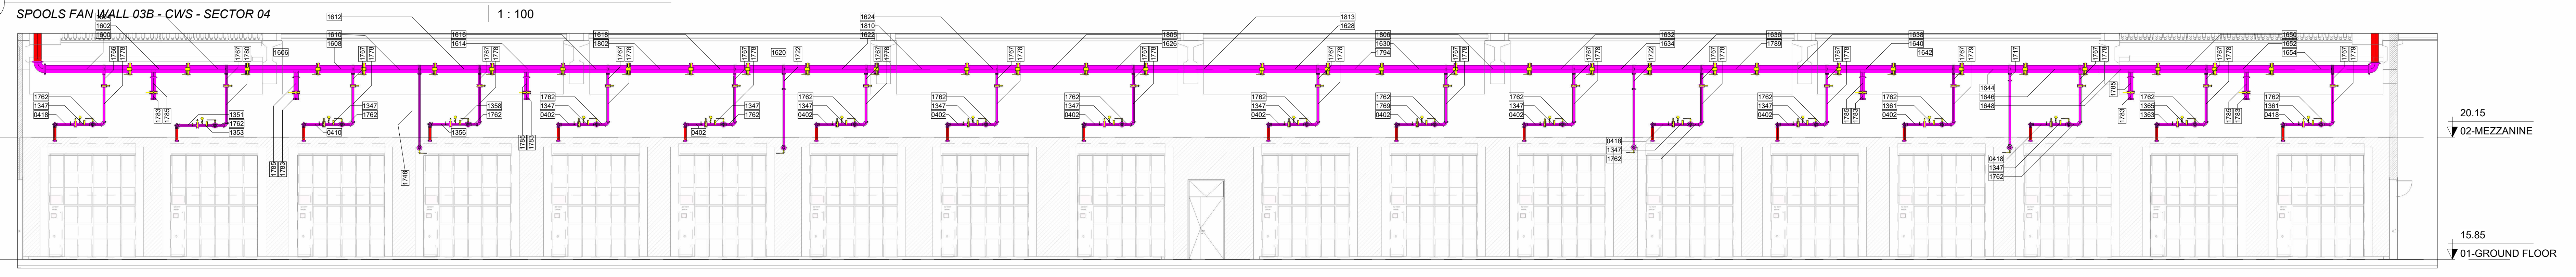
20.15
02-MEZZANINE
15.85
01-GROUND FLOOR

3 — SPO - FAN WALL 03A - RAG - SETOR 04

SPOOLS FAN WALL 03A - CWR - SECTOR 04 | 1 : 100

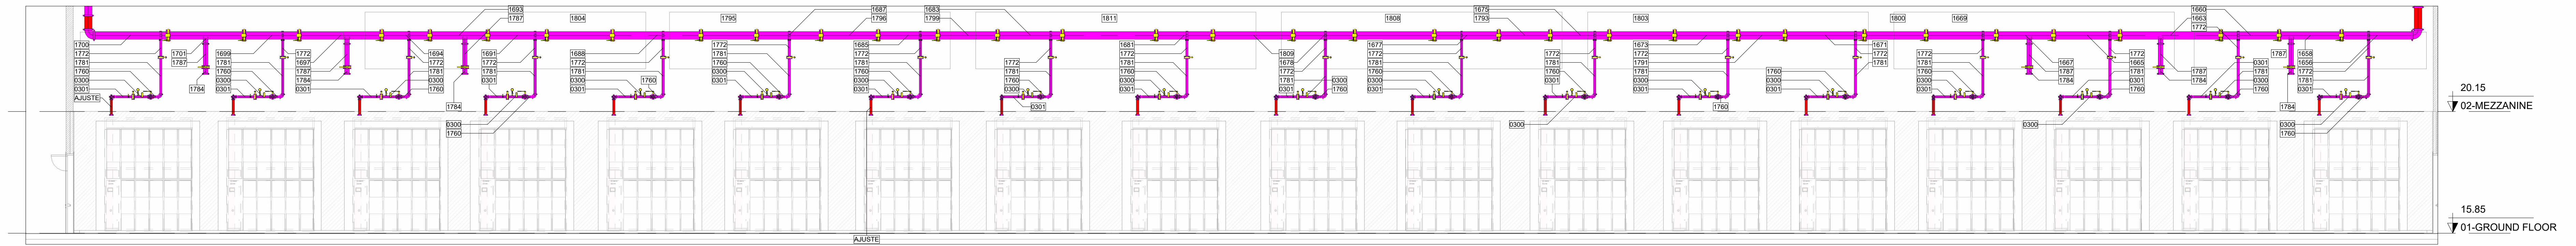
20.15
02-MEZZANINE
15.85
01-GROUND FLOOR

4 — SPO - FAN WALL 03B - RAG - SETOR 04

SPOOLS FAN WALL 03B - CWR - SECTOR 04 | 1 : 100

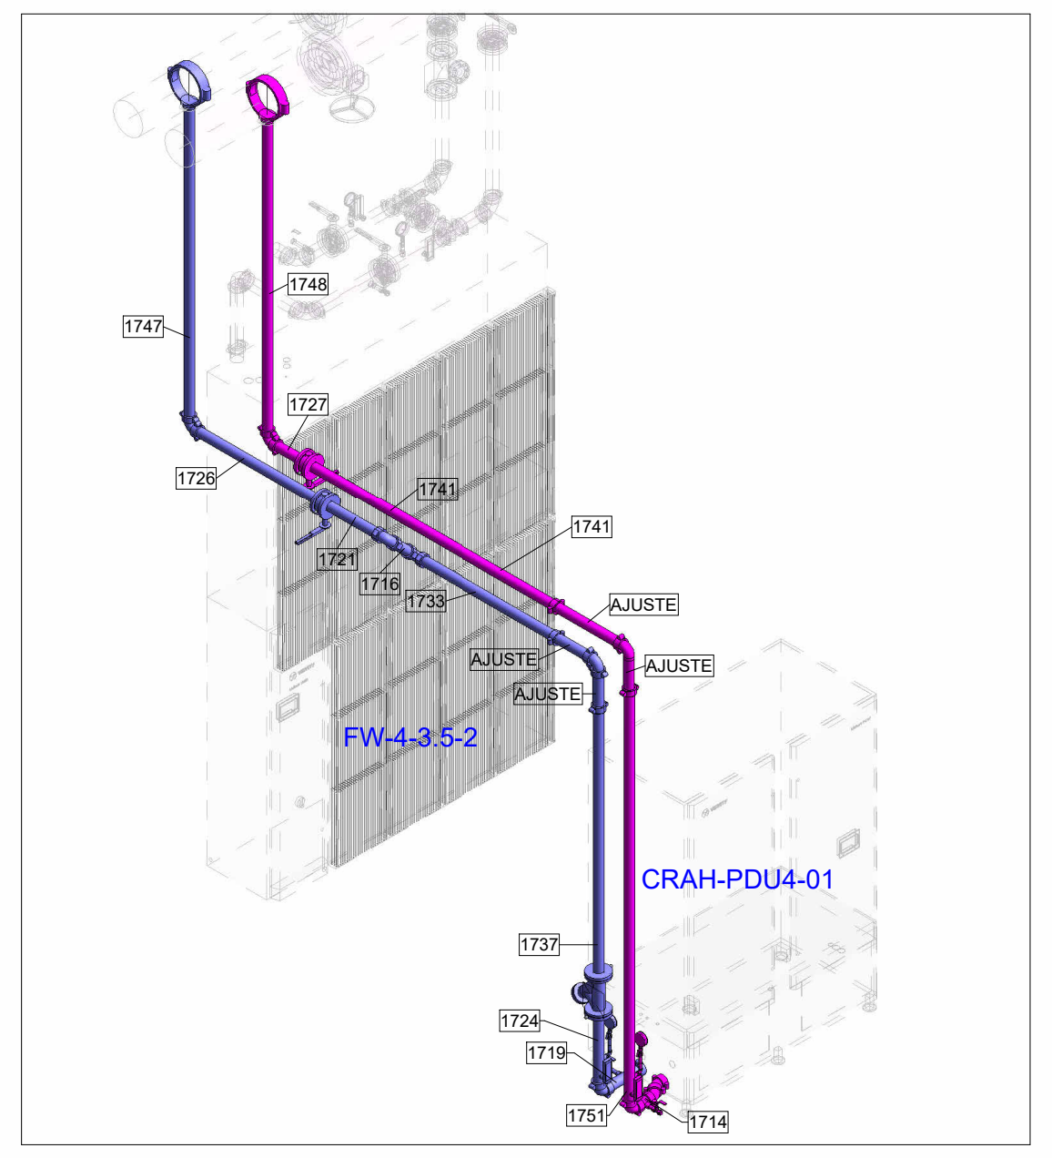
FW-4-3.5-2
CRAH-PDU4-01
AJUSTE

ISOMETRIA - CRAH-PDU4-01 - SETOR 04

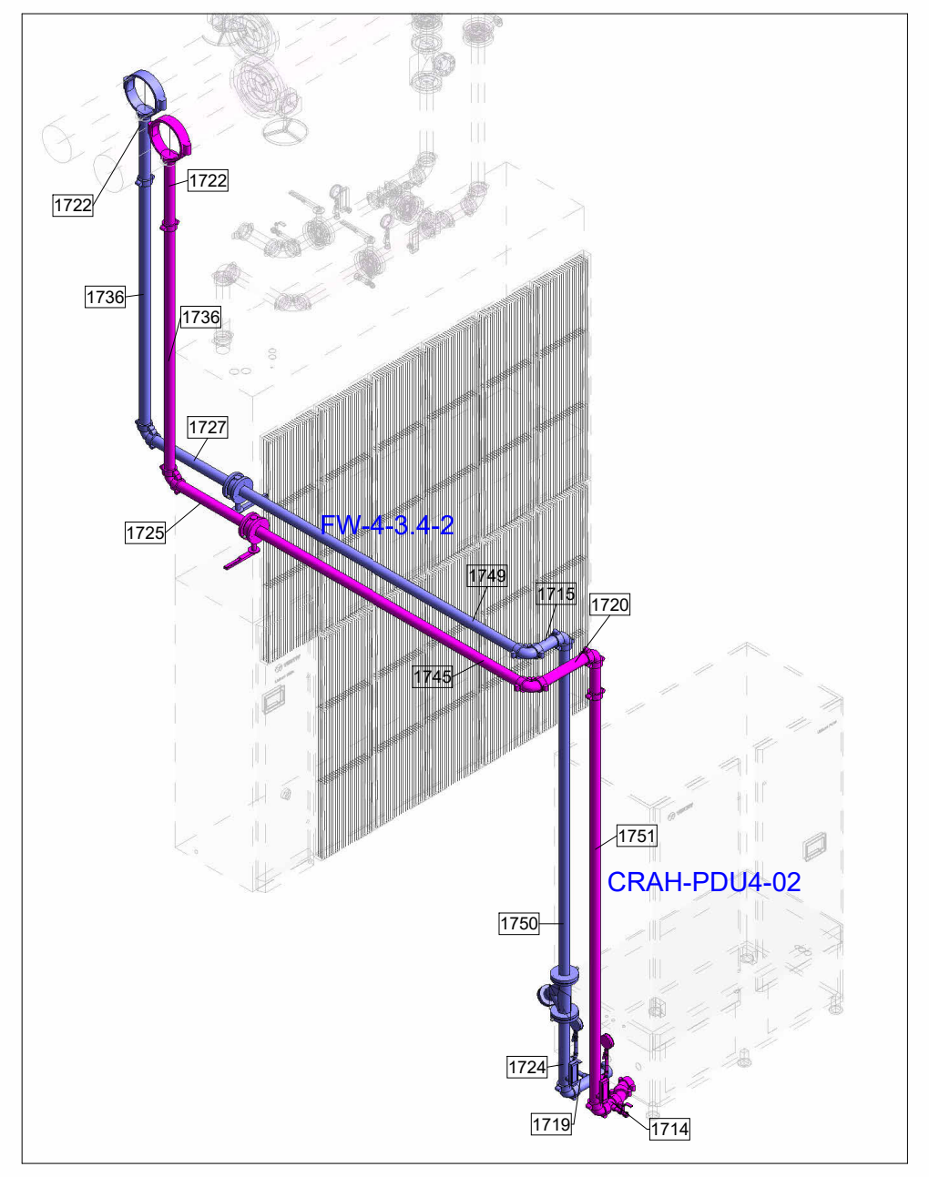
FW-4-3.4-2
CRAH-PDU4-02

ISOMETRIA - CRAH-PDU4-02 - SETOR 04

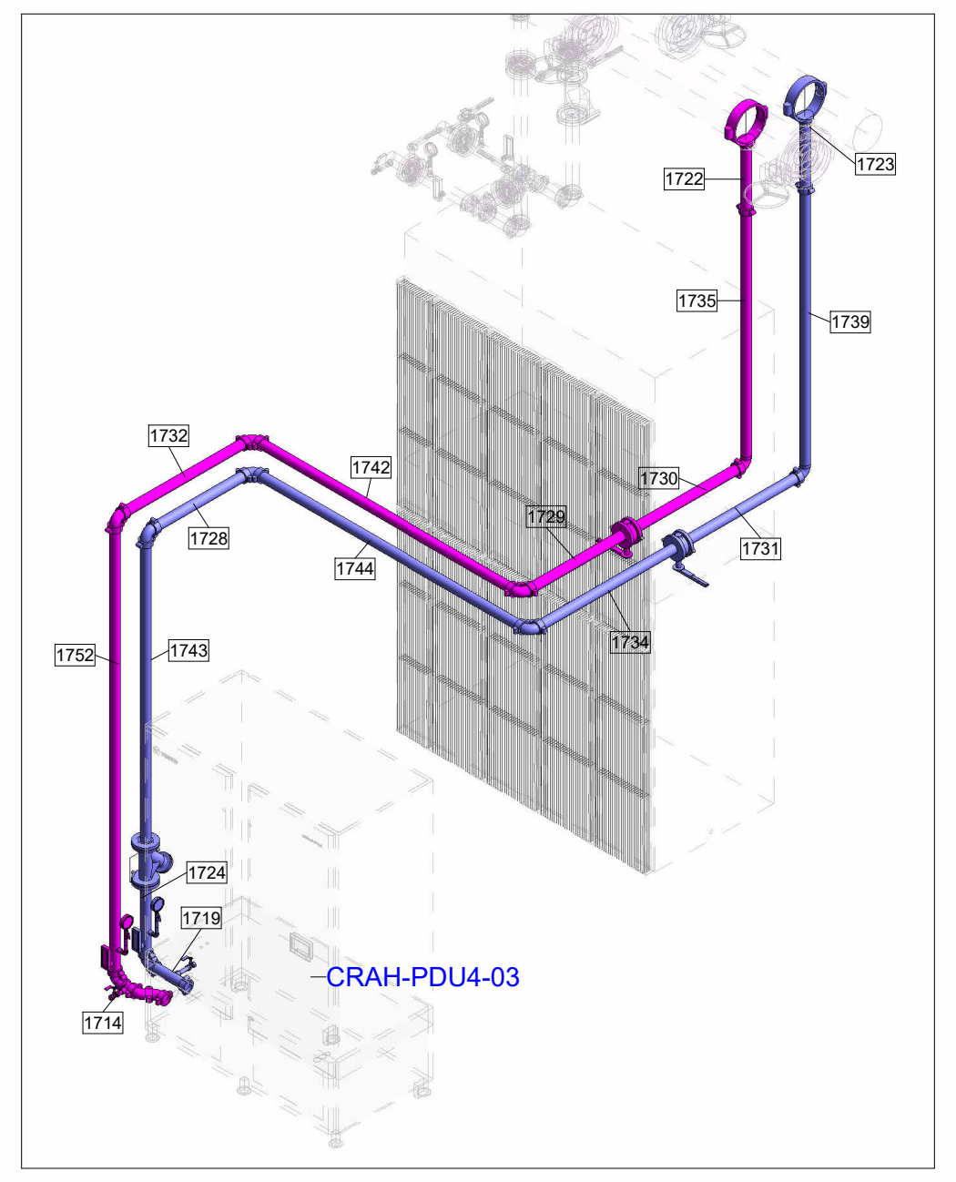
CRAH-PDU4-03

ISOMETRIA - CRAH-PDU4-03 - SETOR 04

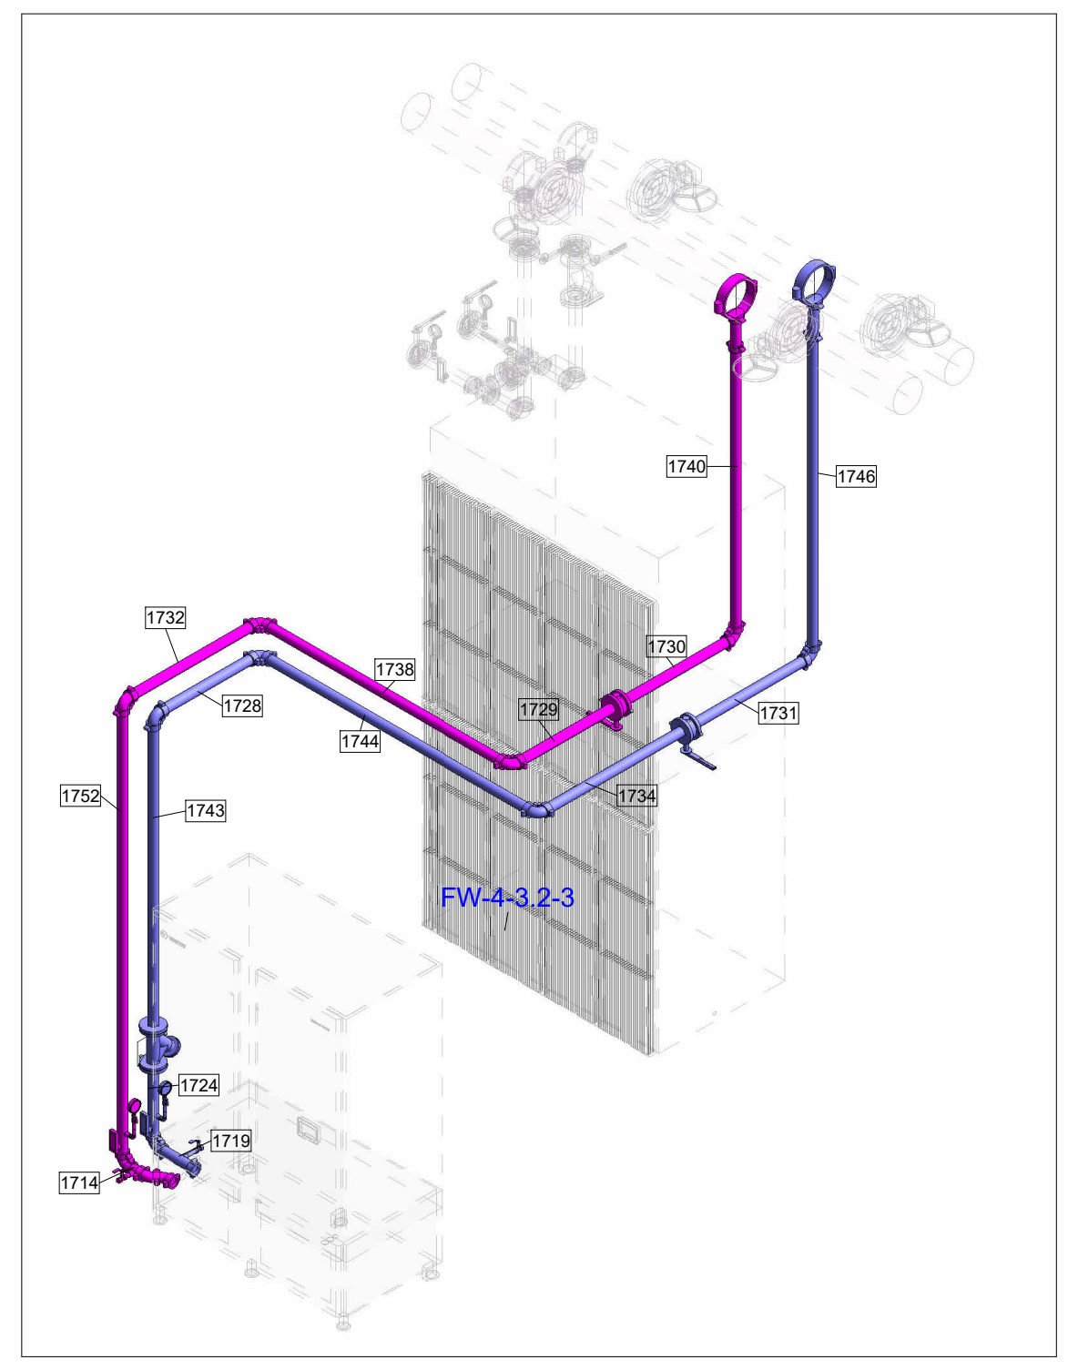

ISOMETRIA - CRAH-PDU4-04 - SETOR 04

LEGENDA / LEGEND:

🟦	AAG - ALIMENTAÇÃO DE ÁGUA GELADA / COLD WATER SUPPLY.
🟪	RAG - RETORNO DE ÁGUA GELADA / COLD WATER RETURN.
🟨	DRENOS / DRAIN.
🟫	TUBULAÇÃO FRIGORÍGENA / REFRIGERANT LINE.
🟥	PEÇA DE AJUSTE / CUT TO FIT. MEDIDAS *IN-LOCO / VERIFY IN FIELD.*

NOTAS TUBULAÇÕES / NOTES PIPING:

1 - MEDIDAS EM MILIMETROS, NÍVEIS EM METROS E TUBULAÇÕES EM POLEGADAS.
DIMENSIONS IN MILLIMETERS, LEVELS IN METERS, AND PIPING IN INCHES.

2 - NÚMEROS ENTRE PARENTESES INDICAM VAZÃO DE ÁGUA EM m³/h.
NUMBERS IN PARENTHESES INDICATE WATER FLOW IN m³/h.

3 - ESPECIFICAÇÃO DE TUBOS:
PIPE SPECIFICATION:

• 1/2" A 2" - Tubo de aço-carbono sem costura ASTM A-106 GR-B, SCH.40, dimensões em ANSI B.36.10, extremidade rosc. BSP • 1/2" TO 2" - Seamless carbon steel pipe ASTM A-106 GR-B, SCH.40, dimensions per ANSI B.36.10, BSP threaded end

• 2 1/2" A 24" - Tubo de aço-carbono com costura ASTM A-106 GR-B, SCH. 40, dimensões em ANSI B.36.10, extremidade ponta reta • 2 1/2" TO 24" - Welded carbon steel pipe ASTM A-106 GR-B, SCH. 40, dimensions per ANSI B.36.10, plain end

4 - PINTURAS: As tubulações devem ser pintadas de acordo com plano de pintura.
PAINTING: Piping shall be painted according to the painting plan.

5 - ISOLAMENTO: deverá ser constituído de espuma elastomérica (classificação T-99).
INSULATION: shall consist of elastomeric foam (classification T-99),

CONSULTAR REF.: 24076-PPC-MD-MEC-DC-10-10-R07 REFER TO REF.: 24076-PPC-MD-MEC-DC-10-10-R07

6 - PEÇAS (SPOOLS) DE AJUSTE : O responsável pela gestão de instalação deverá decidir sobre a necessidade de transformar qualquer SPOOL do projeto em peça de ajuste, a fim de garantir a eficiência e fluidez na montagem além do correto posicionamento do sistema de tubulação.

DESENHOS DE REFERÊNCIA/DRAWING REFERENCES:

DF-TUB-PC13124-0212-1.04 (CADERNO DE FABRICAÇÃO DE SPOOLS), DE-TUB-PC13124-0105-1.04 (ARRANJO DE TUBOS)

PLANTA CHAVE / KEY PLAN:

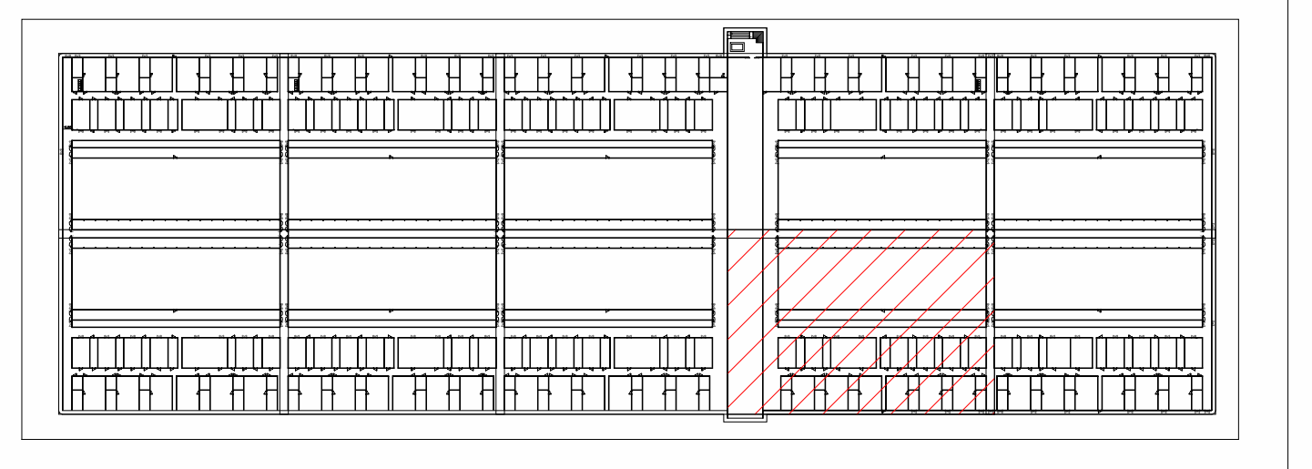

REV. / NO.	DESCRIÇÃO/DESCRIPTION	DATA/DATE	DES./DWN.	APROV./APP.
R00	EMISSÃO INICIAL / INITIAL ISSUE	07/08/2026	RAFAEL T.	RAFAEL

TABELA DE REVISÕES/REVISION SCHEDULE

AFONSO FRANÇA ENGENHARIA

omnia

HEATING COOLING

Rua Mateus de Leão, 116
Cep: 02731-050 - São Paulo
Tel.: +55 11 3931-9900
Email: info@heatingcooling.com.br

ASSUNTO/DESCRIPTION:
TÉRREO/GROUND FLOOR-SETOR 04 - FABRICAÇÃO DE TUBOS CORREDOR FANWALL "A" E "B" / PIPE FABRICATION CORRIDOR FANWALL "A" E "B"

CLIENTE/CLIENT:
DATA CENTER OMNIA DC-01

OBRA/BUILDING:
DATA CENTER OMNIA - DC01

END. OBRA/SITE ADDR:
RODOVIA ESTRUTURANTE CE085, Nº369 - BAIRRO CARAÚBAS - CE

A0L

ESC./SCALE:	DATA/DATE	PROJ./DRAWN BY:	APROV./APPROVAL:
As indicated	06/05/26	RAFAEL T.	DANILO

ARQUIVO/FILE NAME:
DF-TUB-PC13124-0202-1.04-R00.dwg

DES.No./SHEET NO.
DF-TUB-PC13124-0202-1.04

REV.
R00

A0E1 (1374 x 841 mm)